

DISCLAIMER

THESE DRAWINGS ARE PROPERTY OF SAMP ENGINEERING INC. THESE MUST NOT BE REPRODUCED IN WHOLE OR PART. ANY UNAUTHORIZED USE WITHOUT WRITTEN PERMISSION IS PROHIBITED SAMP ENGINEERING INC DISCLAIMS RESPONSIBILITY OF THE DOCUMENTS IF USED IN WHOLE OR PART OF ANY OTHER LOCATION


CONTRACTOR SHOULD REVIEW AND VERIFY ALL DIMENSIONS AND CONDITIONS. CONTRACTOR TO REPORT APPLICANT OF ANY ERROR, OMISSION OR INCONSISTENCY DISCOVERED.

STAMP

REVISION SCHEDULE

NO	DESCRIPTION	DATE

DRAWINGS BY

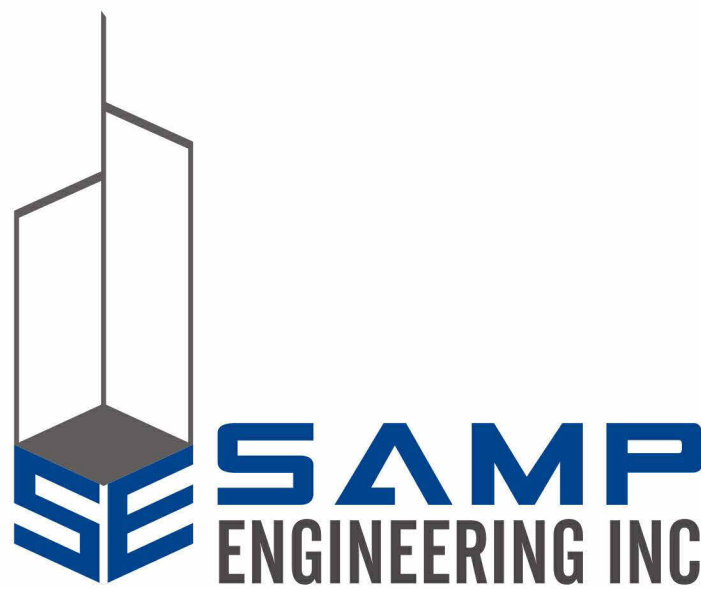

DESCRIPTION

1ST FLOOR COORDINATE PLAN


SCALE: AS SHOWN ON DRAWING

DATE: APRIL 01, 2026

DRAWN BY: DM CHKD BY: KK

DRAWING NO.

DM-03

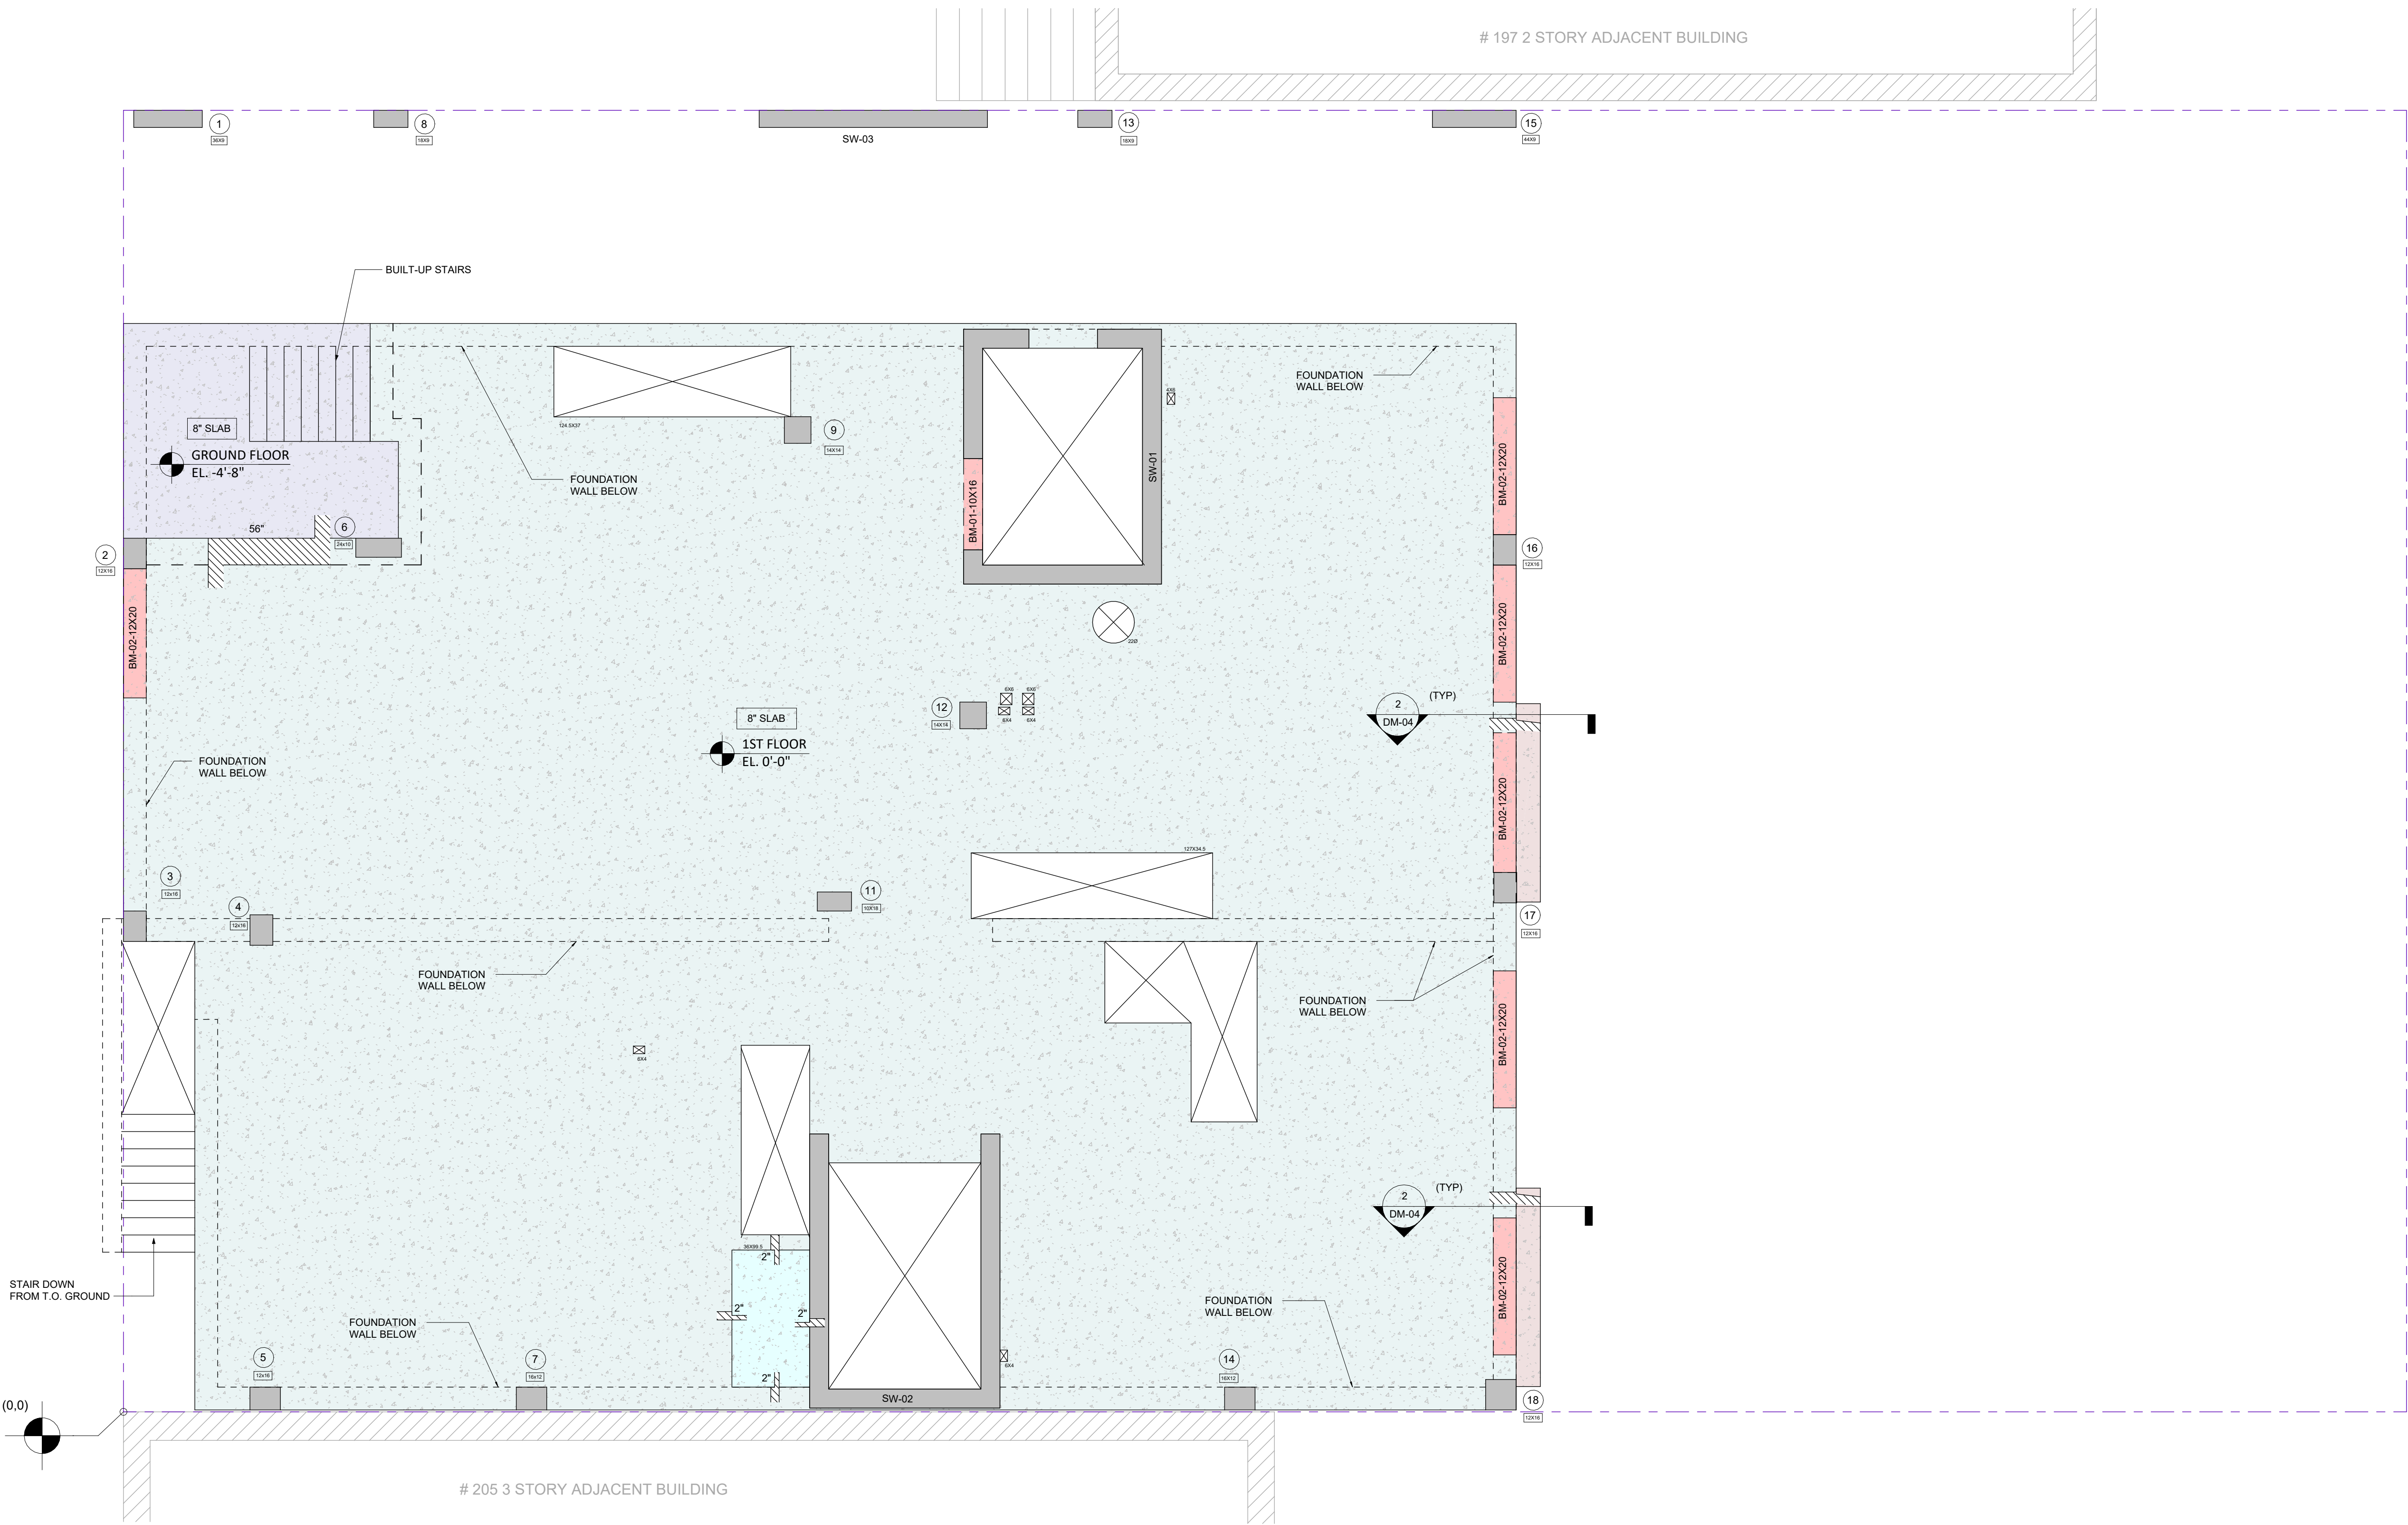

1 1ST FLOOR COORDINATE PLAN
DM-03 1/4" = 1'-0"

LEGEND

- 8" CONC SLAB; EL.-4'8"
- 6" CONC. SLAB; EL.-0'2"
- 8" CONC. SLAB; EL.0'0"
- BEAM
- OPENING
- SHEAR WALL
- COLUMN
- COLUMN SIZE

COORDINATE PLAN

199 NORTH 5TH STEET
BROOKLYN, NY 11211

DISCLAIMER

THESE DRAWINGS ARE PROPERTY OF SAMP ENGINEERING INC. THESE MUST NOT BE REPRODUCED IN WHOLE OR PART. ANY UNAUTHORIZED USE WITHOUT WRITTEN PERMISSION IS PROHIBITED SAMP ENGINEERING INC DISCLAIMS RESPONSIBILITY OF THE DOCUMENTS IF USED IN WHOLE OR PART OF ANY OTHER LOCATION


CONTRACTOR SHOULD REVIEW AND VERIFY ALL DIMENSIONS AND CONDITIONS. CONTRACTOR TO REPORT APPLICANT OF ANY ERROR, OMISSION OR INCONSISTENCY DISCOVERED.

STAMP

REVISION SCHEDULE

NO	DESCRIPTION	DATE

DRAWINGS BY

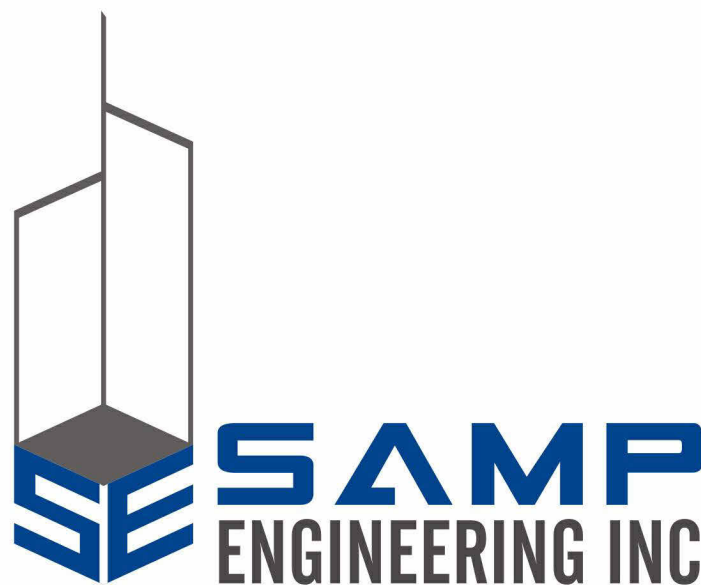

DESCRIPTION

1ST FLOOR COORDINATE
PLAN


SCALE: AS SHOWN ON DRAWING

DATE: APRIL 01, 2026

DRAWN BY: DM CHKD BY: KK

DRAWING NO.

DM-03

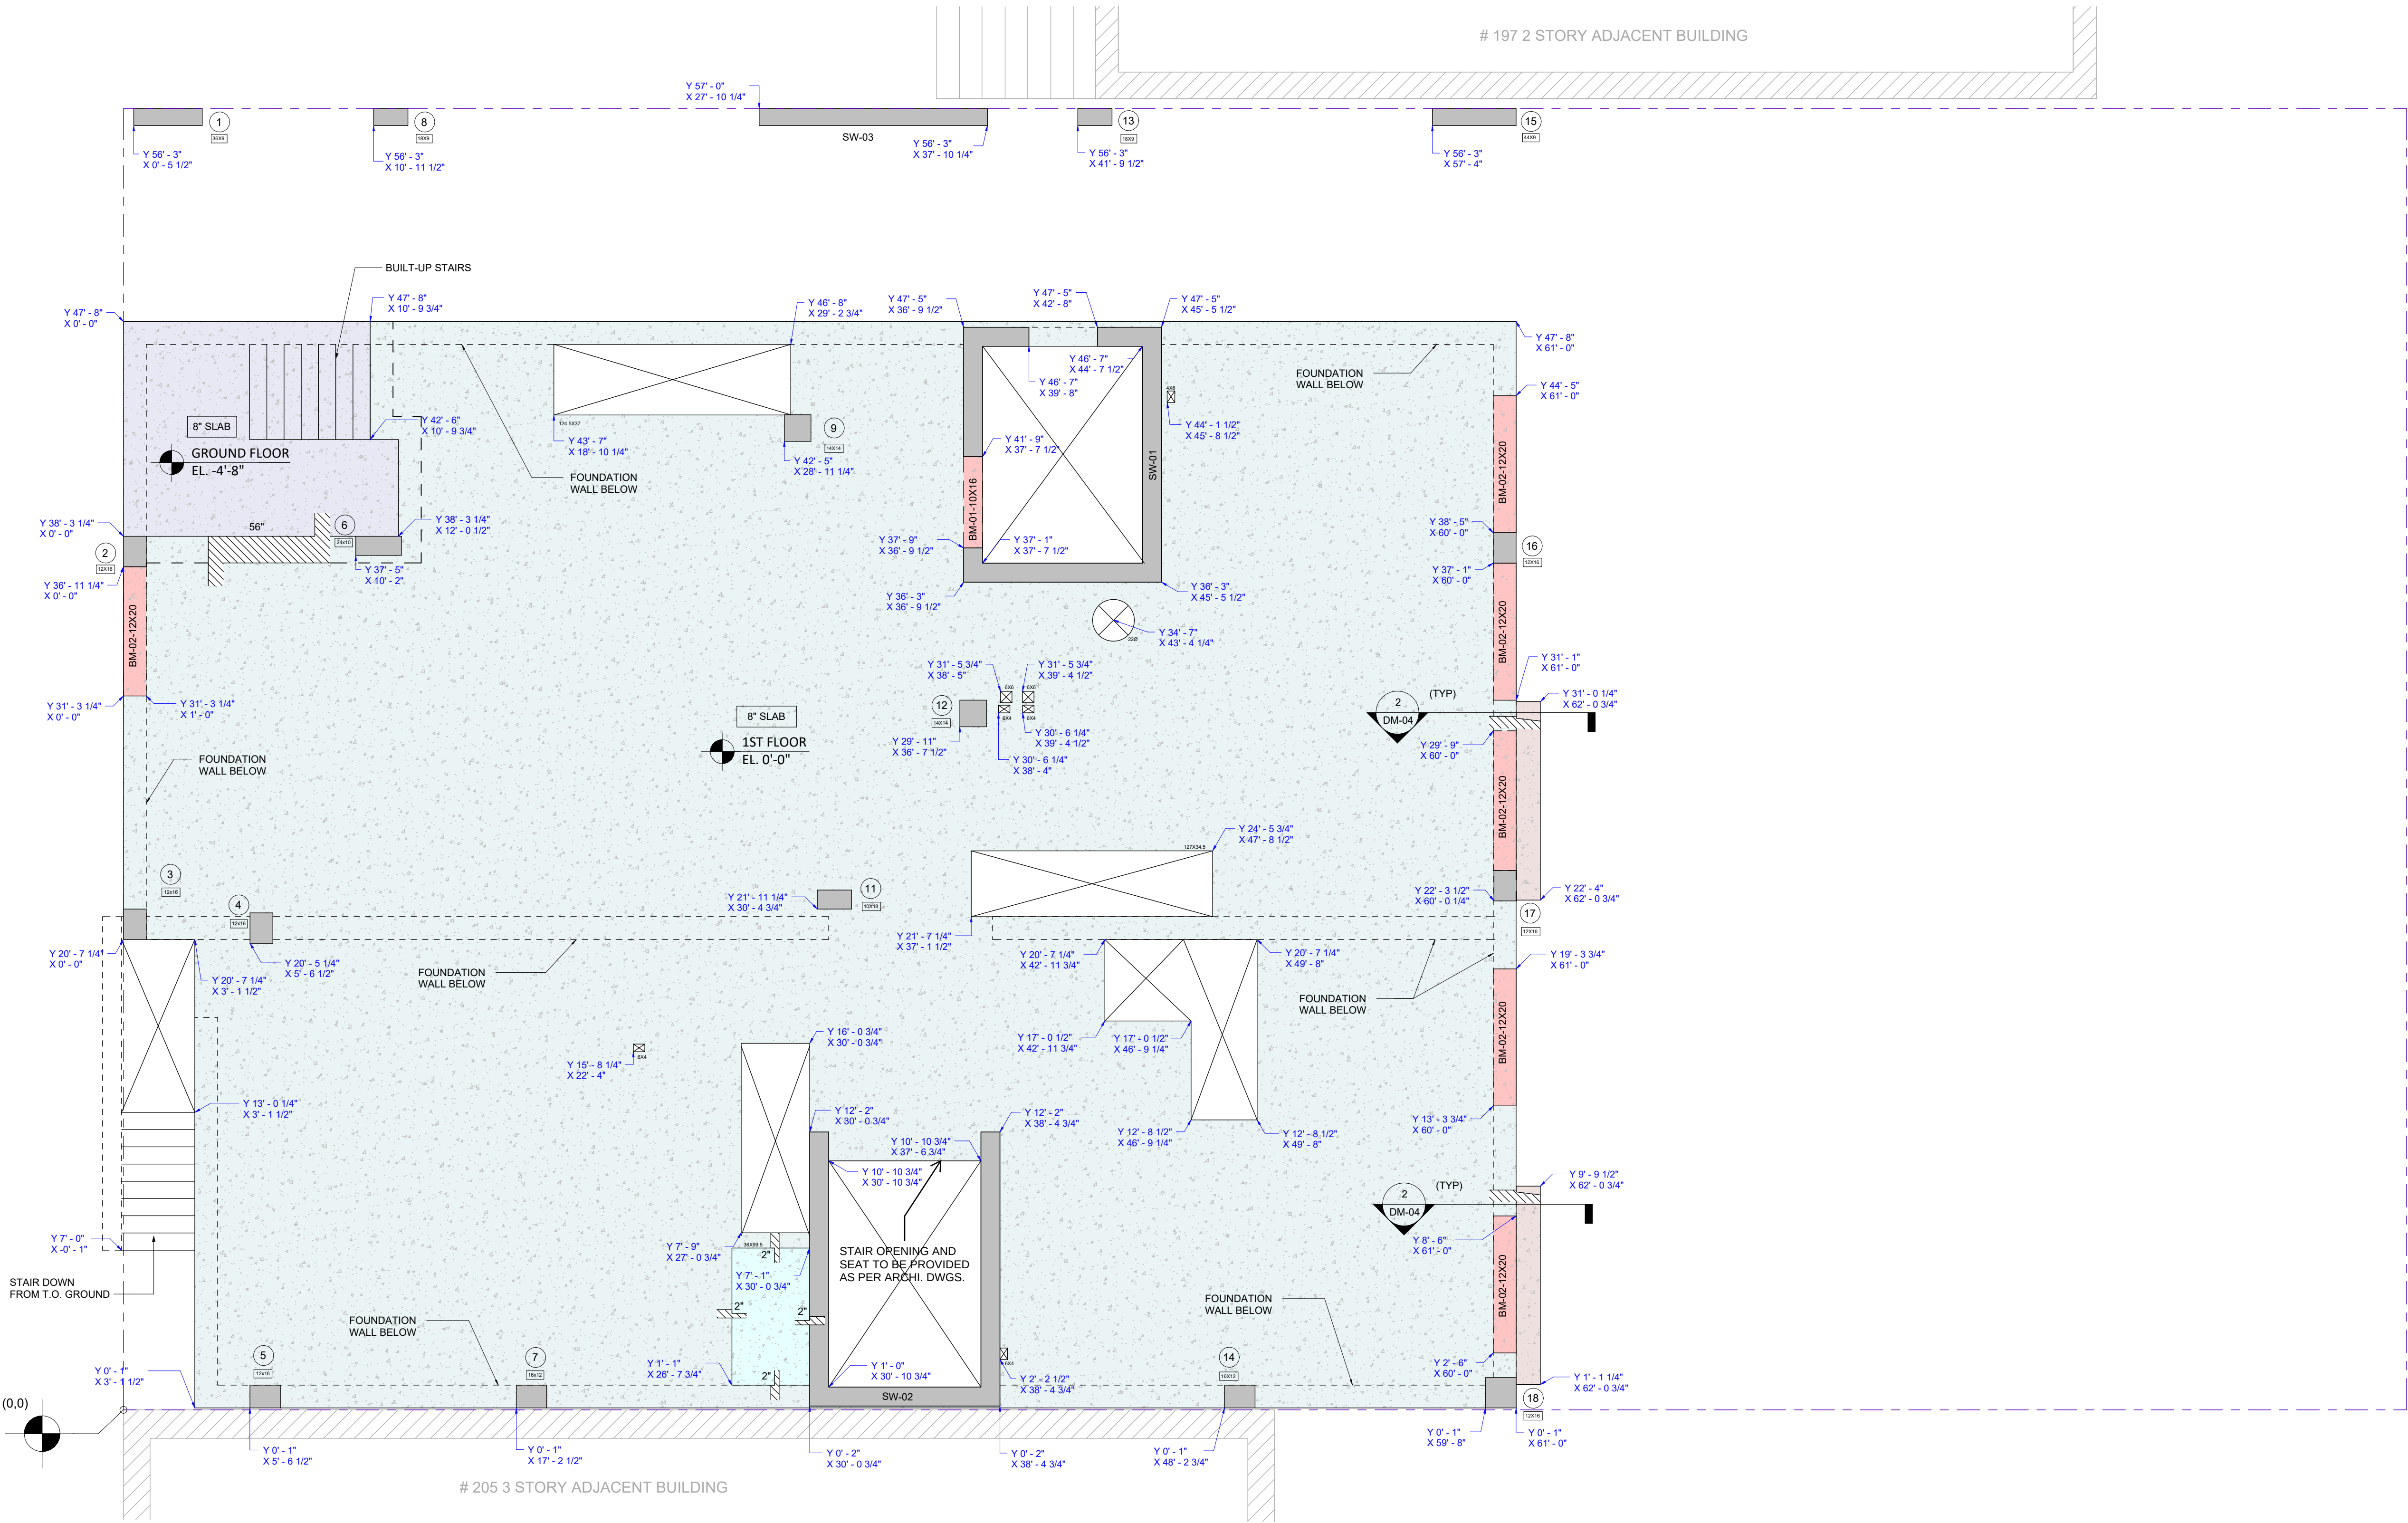

NOTES:

- CONTRACTOR TO VERIFY ALL COORDINATES, DIMENSIONS AND ELEVATIONS BEFORE USING THESE DRAWINGS.
- THESE DRAWINGS ARE BASED ON STRUCTURE DRAWINGS DATED 01/27/2026

LEGEND

- 8" CONC SLAB; EL.-4'8"
- 6" CONC. SLAB; EL.-0'2"
- 8" CONC. SLAB; EL.0'0"
- BEAM
- OPENING
- SW-XX SHEAR WALL
- XX COLUMN
- L x B COLUMN SIZE

DIMENSION PLAN

199 NORTH 5TH STEET
BROOKLYN, NY 11211

DISCLAIMER

THESE DRAWINGS ARE PROPERTY OF SAMP ENGINEERING INC. THESE MUST NOT BE REPRODUCED IN WHOLE OR PART. ANY UNAUTHORIZED USE WITHOUT WRITTEN PERMISSION IS PROHIBITED SAMP ENGINEERING INC DISCLAIMS RESPONSIBILITY OF THE DOCUMENTS IF USED IN WHOLE OR PART OF ANY OTHER LOCATION


CONTRACTOR SHOULD REVIEW AND VERIFY ALL DIMENSIONS AND CONDITIONS. CONTRACTOR TO REPORT APPLICANT OF ANY ERROR, OMISSION OR INCONSISTENCY DISCOVERED.

STAMP

REVISION SCHEDULE

NO	DESCRIPTION	DATE

DRAWINGS BY

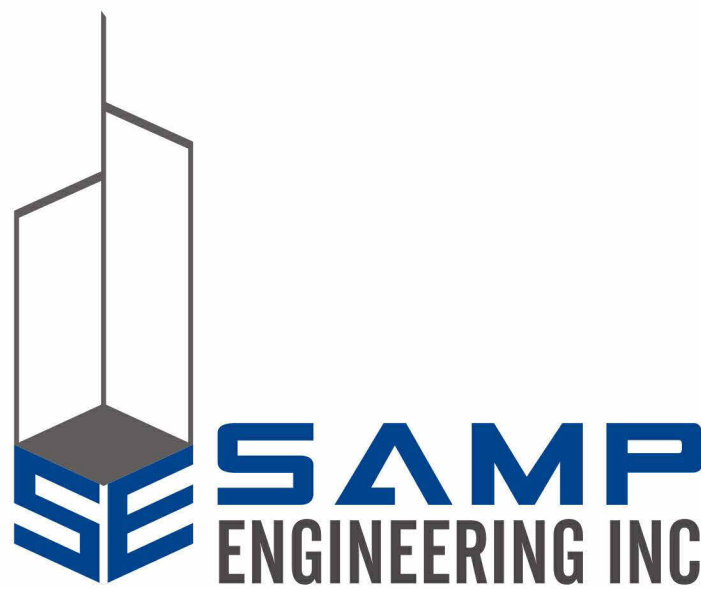

DESCRIPTION

1ST FLOOR DIMENSION PLAN


SCALE: AS SHOWN ON DRAWING

DATE: APRIL 01, 2026


DRAWN BY: DM CHKD BY: KK

DRAWING NO.

DM-04

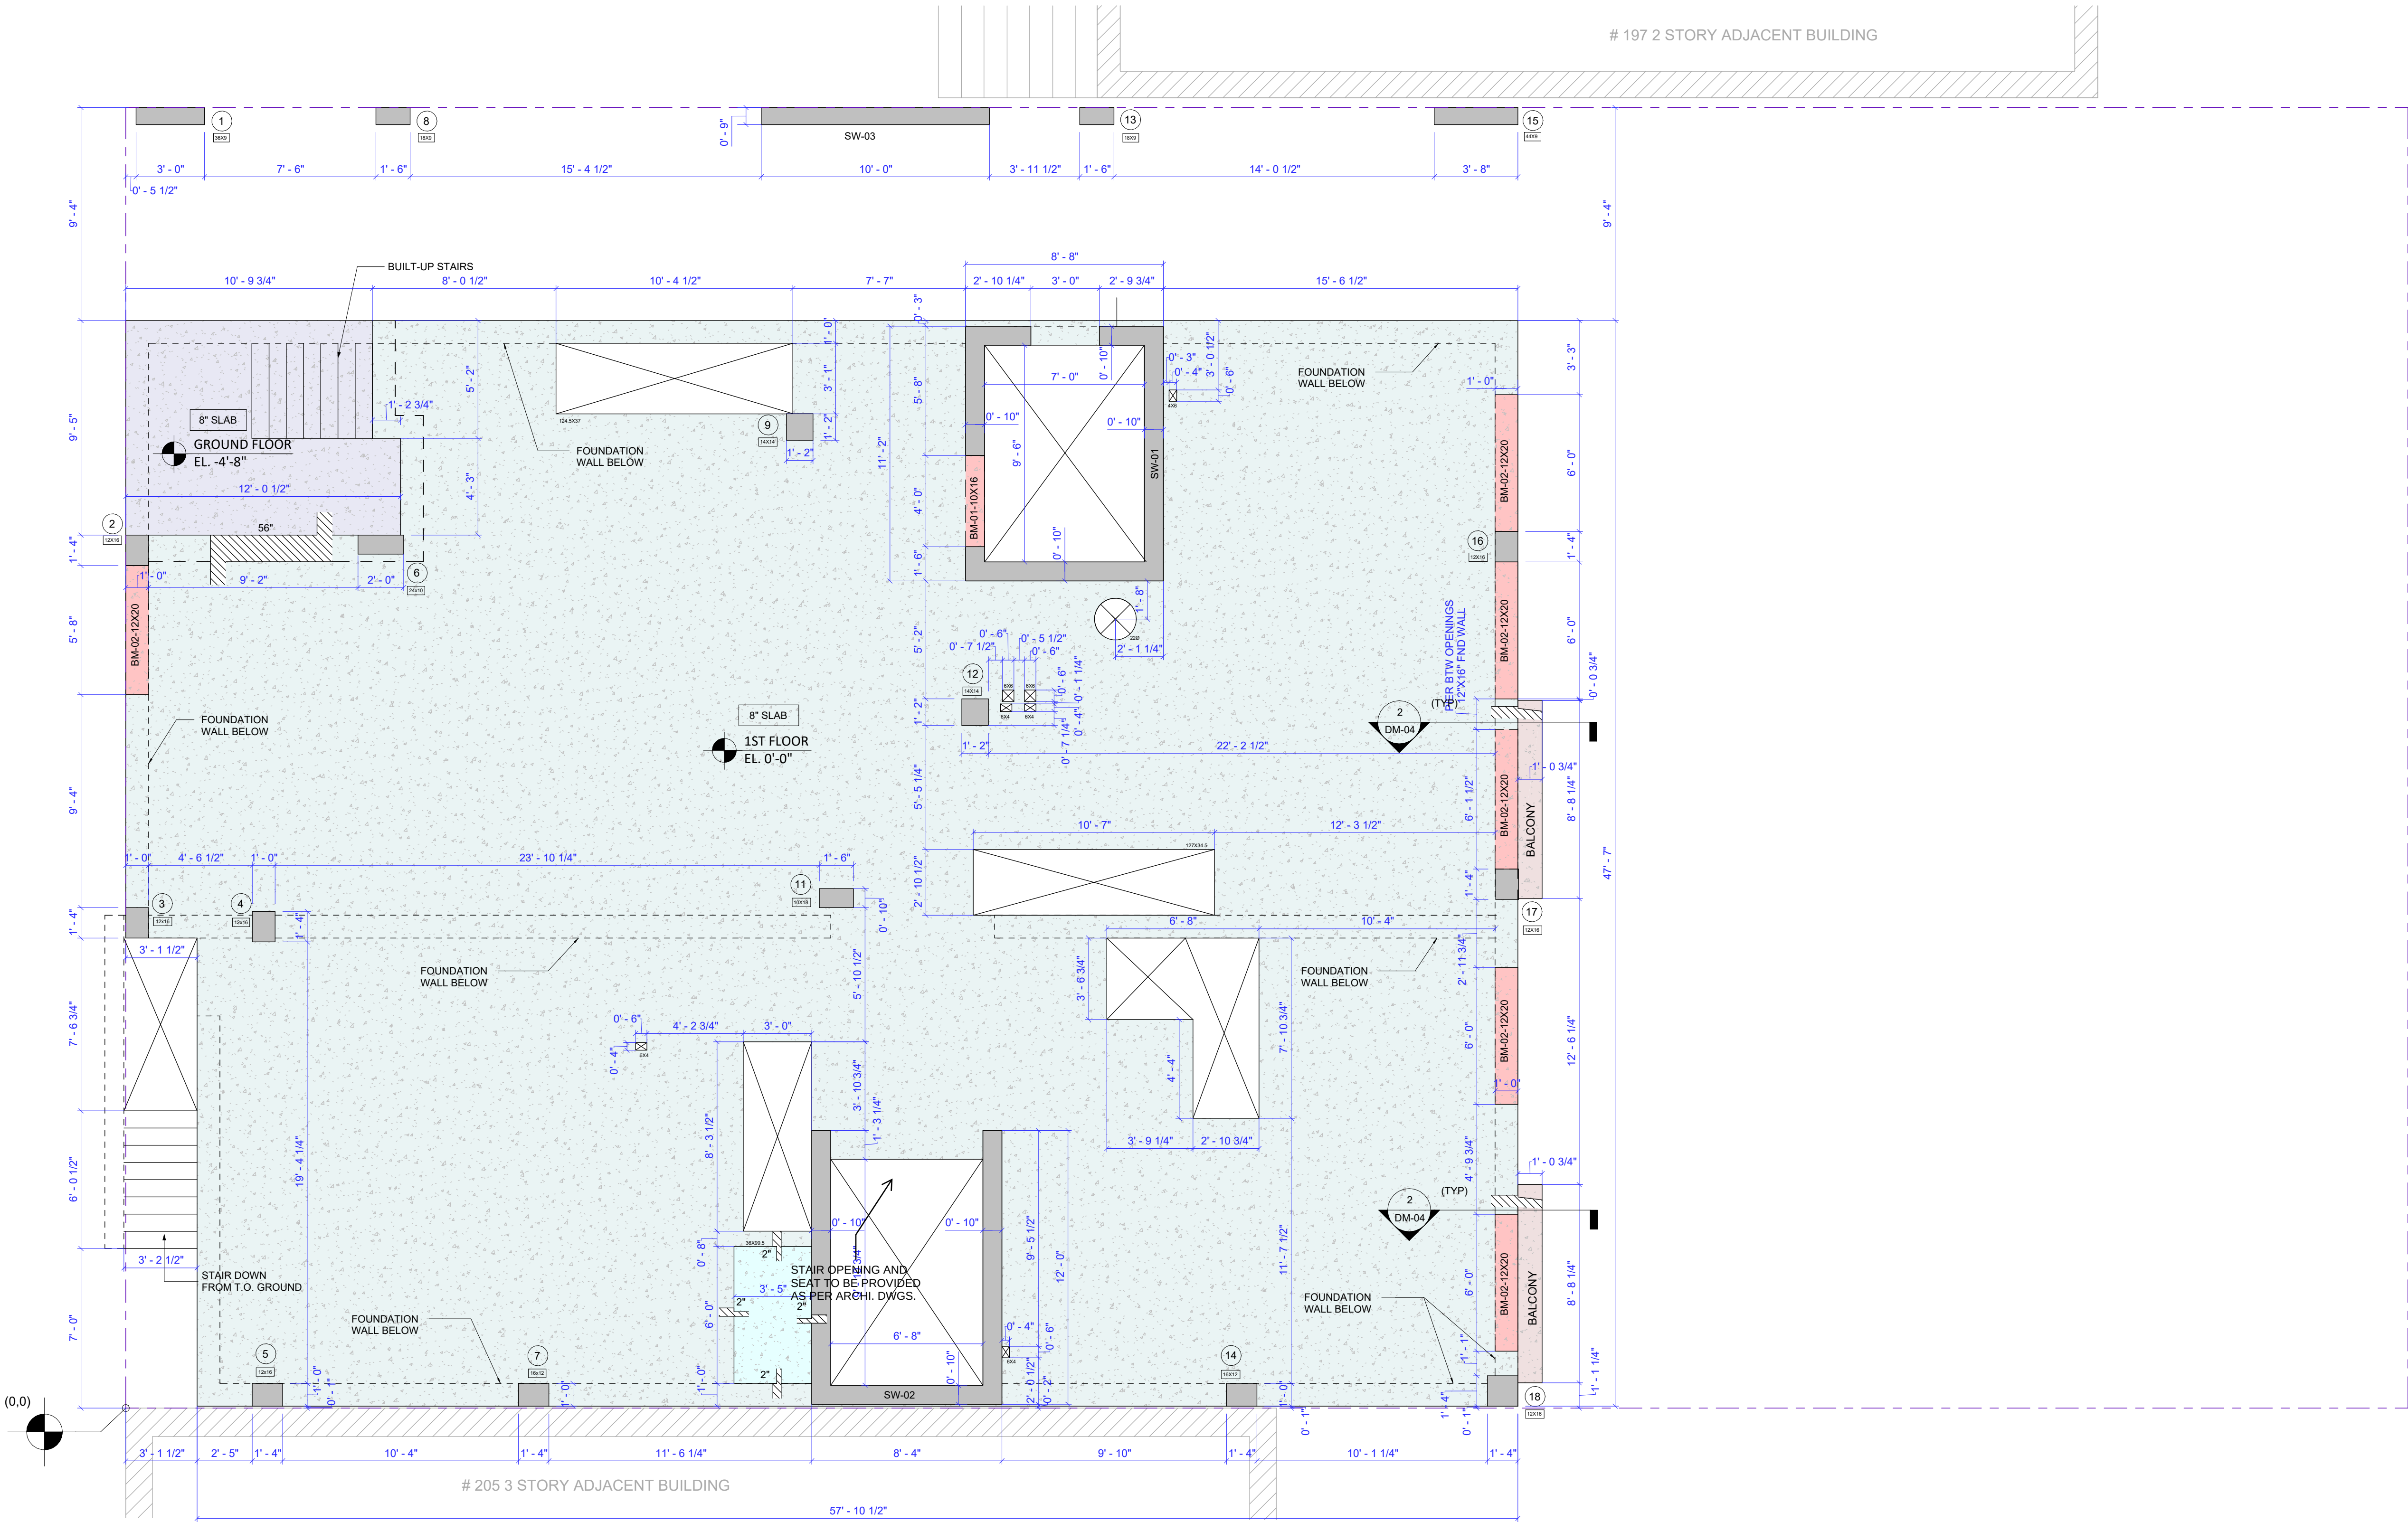

1 1ST FLOOR DIMENSION PLAN
1/4" = 1'-0"

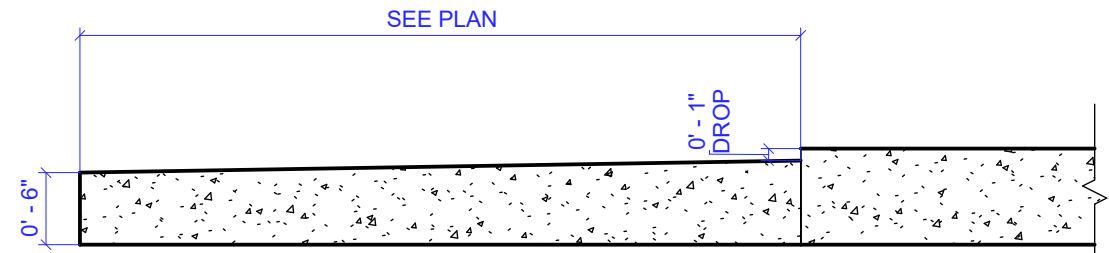

2 TYPICAL SECTION AT BALCONIES
DM-04 N.T.S

LEGEND

- 8" CONC SLAB; EL.-4'8"
- 6" CONC. SLAB; EL.-0'2"
- 8" CONC. SLAB; EL.0'0"
- BEAM
- OPENING
- SW-XX SHEAR WALL
- XX COLUMN
- L x B COLUMN SIZE